


REFER TO FRDPD02-EDC-65-00-DR-E-006501

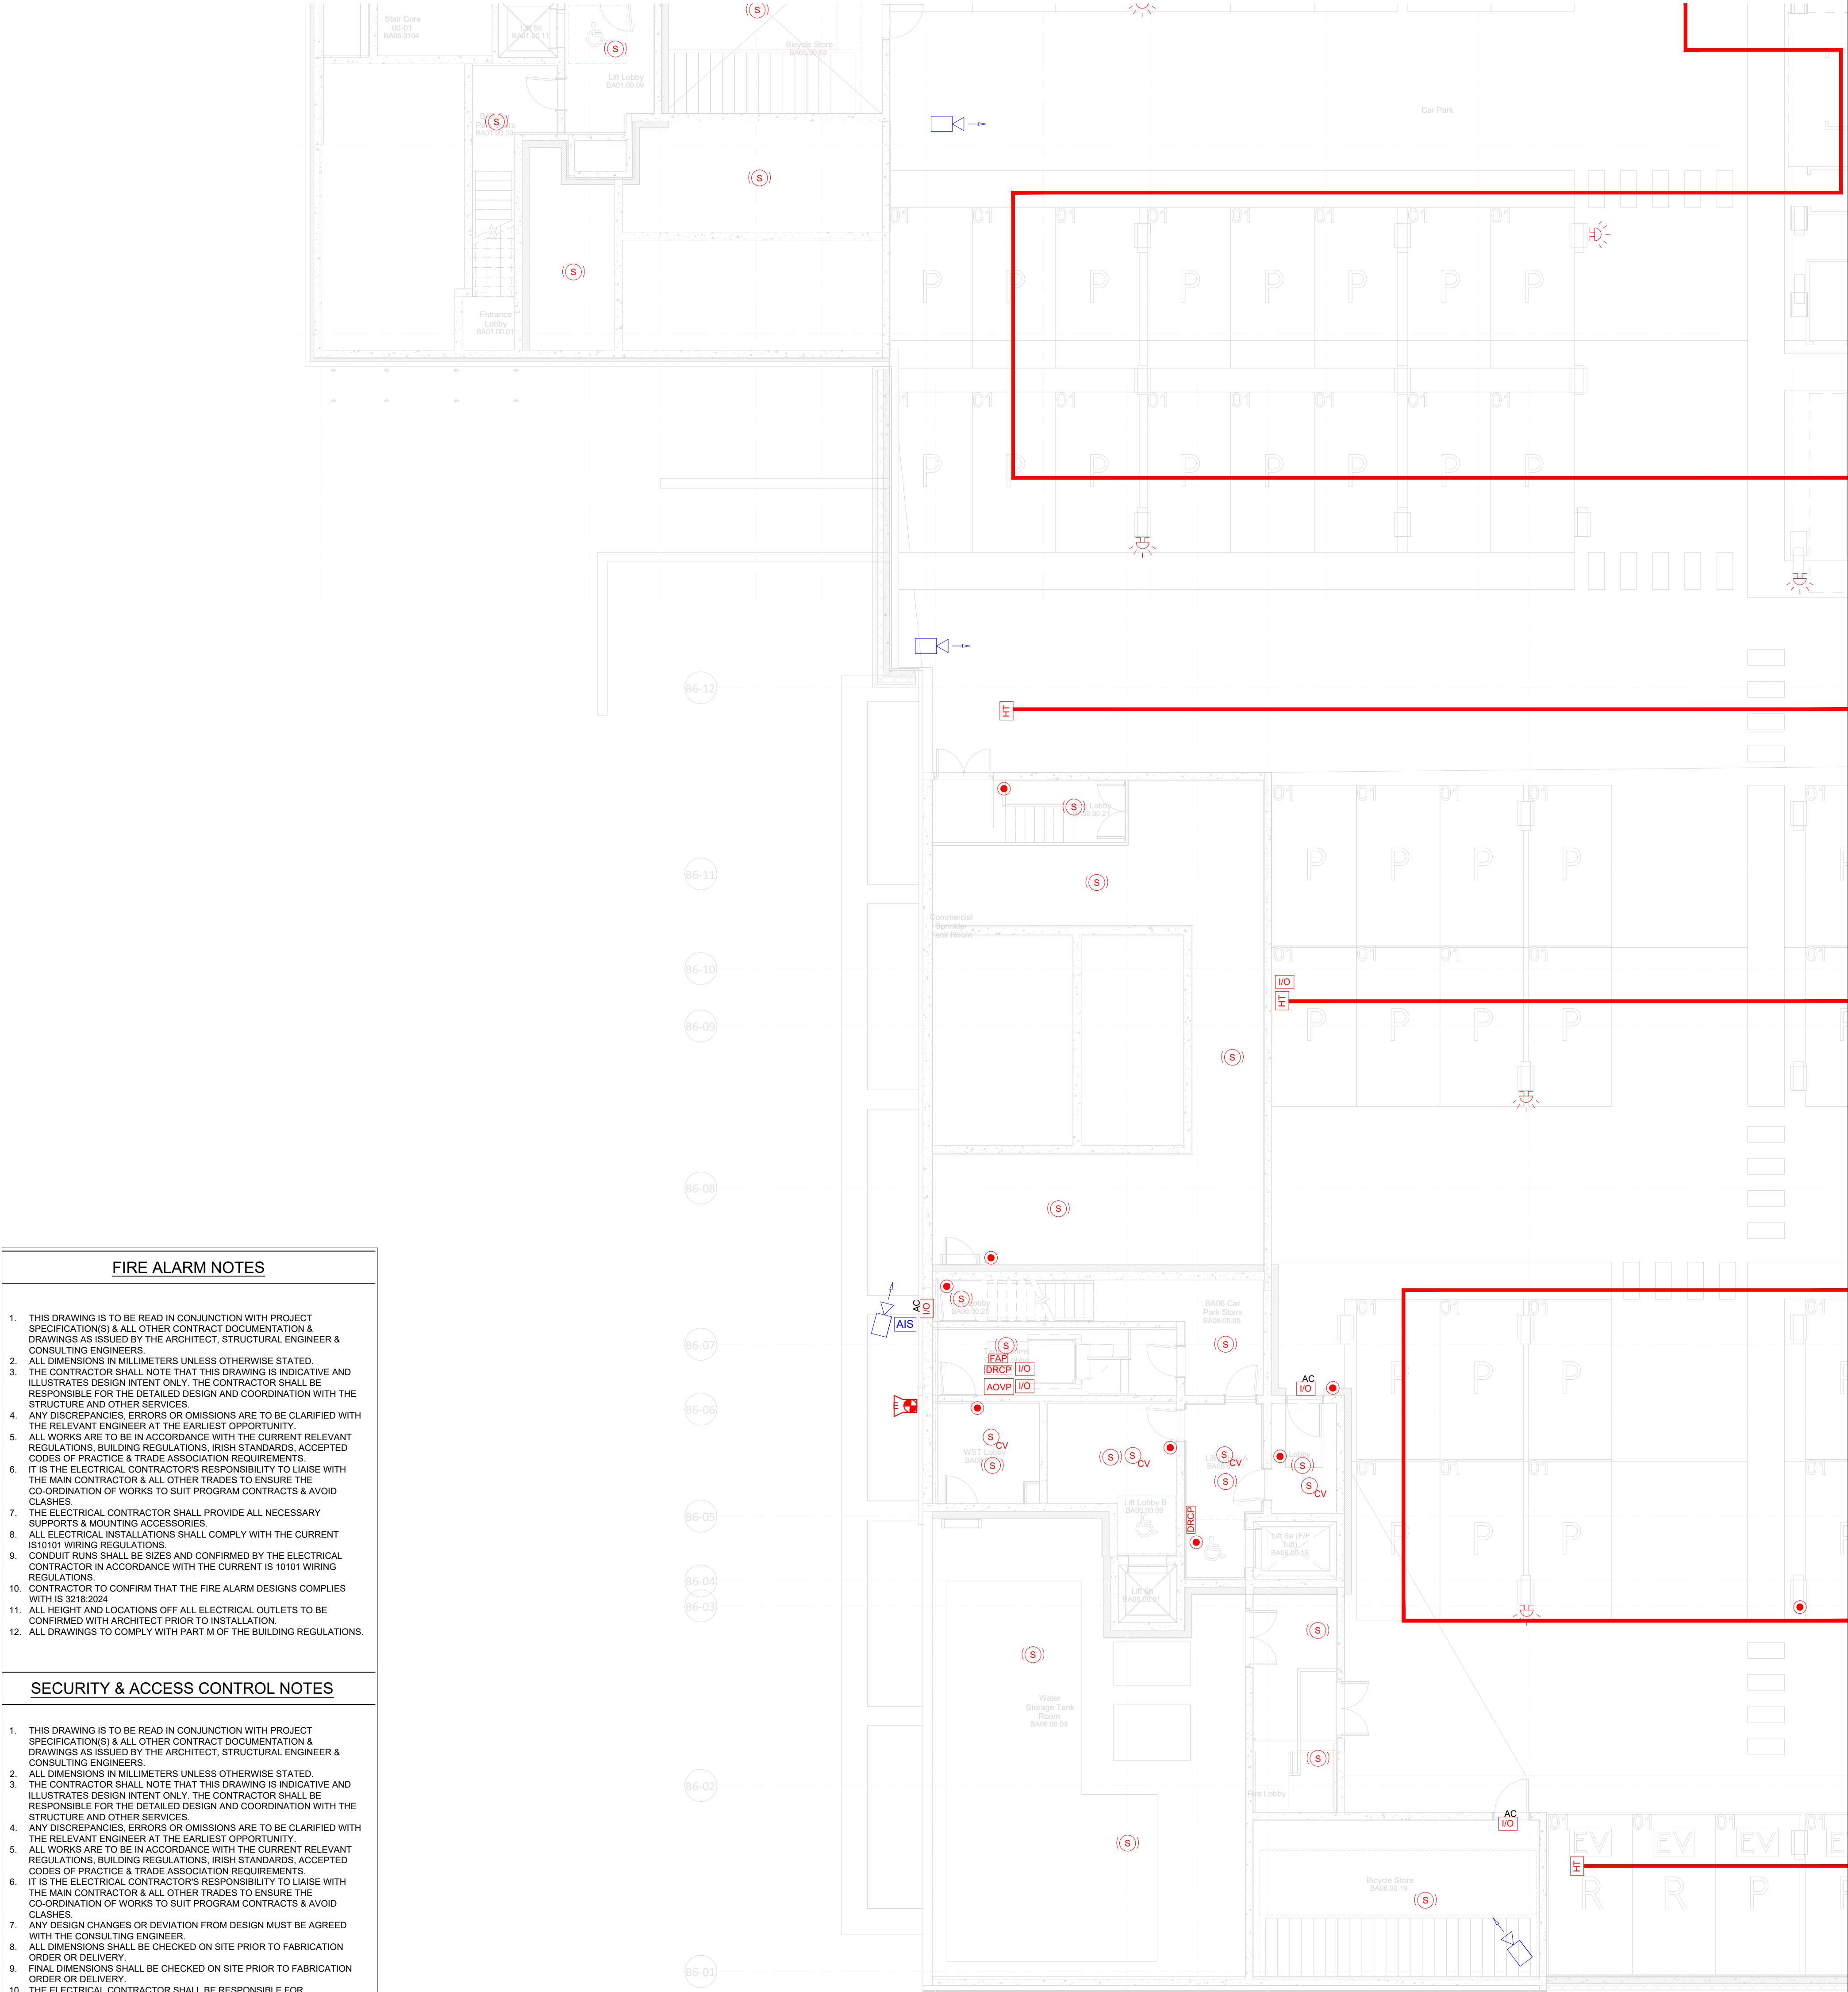

REFER TO FRDPD02-EDC-65-00-DR-E-006504

FIRE ALARM NOTES

1. THIS DRAWING IS TO BE READ IN CONJUNCTION WITH PROJECT SPECIFICATION(S) & ALL OTHER CONTRACT DOCUMENTATION & DRAWINGS AS ISSUED BY THE ARCHITECT, STRUCTURAL ENGINEER & CONSULTING ENGINEERS.
2. ALL DIMENSIONS IN MILLIMETERS UNLESS OTHERWISE STATED.
3. THE CONTRACTOR SHALL NOTE THAT THIS DRAWING IS INDICATIVE AND ILLUSTRATES DESIGN INTENT ONLY. THE CONTRACTOR SHALL BE RESPONSIBLE FOR THE DETAILED DESIGN AND COORDINATION WITH THE STRUCTURE AND OTHER SERVICES.
4. ANY DISCREPANCIES, ERRORS OR OMISSIONS ARE TO BE CLARIFIED WITH THE RELEVANT ENGINEER AT THE EARLIEST OPPORTUNITY.
5. ALL WORKS ARE TO BE IN ACCORDANCE WITH THE CURRENT RELEVANT REGULATIONS, BUILDING REGULATIONS, IRISH STANDARDS, ACCEPTED CODES OF PRACTICE & TRADE ASSOCIATION REQUIREMENTS.
6. IT IS THE ELECTRICAL CONTRACTOR'S RESPONSIBILITY TO LIAISE WITH THE MAIN CONTRACTOR & ALL OTHER TRADES TO ENSURE THE CO-ORDINATION OF WORKS TO SUIT PROGRAM CONTRACTS & AVOID CLASHES.
7. THE ELECTRICAL CONTRACTOR SHALL PROVIDE ALL NECESSARY SUPPORTS & MOUNTING ACCESSORIES.
8. ALL ELECTRICAL INSTALLATIONS SHALL COMPLY WITH THE CURRENT IS10101 WIRING REGULATIONS.
9. CONDUIT RUNS SHALL BE SIZES AND CONFIRMED BY THE ELECTRICAL CONTRACTOR IN ACCORDANCE WITH THE CURRENT IS 10101 WIRING REGULATIONS.
10. CONTRACTOR TO CONFIRM THAT THE FIRE ALARM DESIGNS COMPLIES WITH IS 5218:2024
11. ALL HEIGHT AND LOCATIONS OFF ALL ELECTRICAL OUTLETS TO BE CONFIRMED WITH ARCHITECT PRIOR TO INSTALLATION.
12. ALL DRAWINGS TO COMPLY WITH PART M OF THE BUILDING REGULATIONS.

SECURITY & ACCESS CONTROL NOTES

1. THIS DRAWING IS TO BE READ IN CONJUNCTION WITH PROJECT SPECIFICATION(S) & ALL OTHER CONTRACT DOCUMENTATION & DRAWINGS AS ISSUED BY THE ARCHITECT, STRUCTURAL ENGINEER & CONSULTING ENGINEERS.
2. ALL DIMENSIONS IN MILLIMETERS UNLESS OTHERWISE STATED.
3. THE CONTRACTOR SHALL NOTE THAT THIS DRAWING IS INDICATIVE AND ILLUSTRATES DESIGN INTENT ONLY. THE CONTRACTOR SHALL BE RESPONSIBLE FOR THE DETAILED DESIGN AND COORDINATION WITH THE STRUCTURE AND OTHER SERVICES.
4. ANY DISCREPANCIES, ERRORS OR OMISSIONS ARE TO BE CLARIFIED WITH THE RELEVANT ENGINEER AT THE EARLIEST OPPORTUNITY.
5. ALL WORKS ARE TO BE IN ACCORDANCE WITH THE CURRENT RELEVANT REGULATIONS, BUILDING REGULATIONS, IRISH STANDARDS, ACCEPTED CODES OF PRACTICE & TRADE ASSOCIATION REQUIREMENTS.
6. IT IS THE ELECTRICAL CONTRACTOR'S RESPONSIBILITY TO LIAISE WITH THE MAIN CONTRACTOR & ALL OTHER TRADES TO ENSURE THE CO-ORDINATION OF WORKS TO SUIT PROGRAM CONTRACTS & AVOID CLASHES.
7. ANY DESIGN CHANGES OR DEVIATION FROM DESIGN MUST BE AGREED WITH THE CONSULTING ENGINEER.
8. ALL DIMENSIONS SHALL BE CHECKED ON SITE PRIOR TO FABRICATION ORDER OR DELIVERY.
9. FINAL DIMENSIONS SHALL BE CHECKED ON SITE PRIOR TO FABRICATION ORDER OR DELIVERY.
10. THE ELECTRICAL CONTRACTOR SHALL BE RESPONSIBLE FOR COORDINATION OF ALL SERVICES ON SITE.
11. ALL DRAWINGS TO BE IN CONJUNCTION WITH ARCHITECTURAL DRAWINGS.
12. THE CONTRACTOR SHALL ALLOW FOR ALL NECESSARY SUPPORTS AND FITTINGS REQUIRED TO PROVIDE A FULLY FUNCTIONING INSTALLATION.
13. FINAL LOCATIONS OF ALL ACCESS CONTROL EQUIPMENT SUBJECT TO CONTRACTOR ARRANGING A SITE VISIT WITH SPECIALIST.
14. CCTV LOCATIONS SHOWN ARE INDICATIVE ONLY. CCTV SPECIALIST TO POSITION CAMERAS FOR BEST AREA COVERAGE BASED ON NUMBERS.

LEGEND

- INPUT OUTPUT DEVICES
- BREAK GLASS MANUAL CALL POINT
- FLASHING BEACON
- CO2 DETECTOR
- SMOKE DETECTOR
- HEAT DETECTOR


- SMOKE DETECTOR BEACON
- SMOKE DETECTOR CV COMPLETE WITH RI
- SMOKE SOUNDER
- HEAT DETECTOR SOUNDER
- HEAT DETECTOR BEACON SOUNDER
- SMOKE DETECTOR BEACON SOUNDER

- SOUNDER FLASHING BEACON
- FIRE ALARM REPEATER PANEL
- FIRE ALARM PANEL
- POWER SUPPLY UNIT
- FIRE ALARM SOUNDER
- AOV CALL POINT

- DISABLE PULLCORD
- DISABLE ALARM RESET
- OVERDOOR INDICATOR LAMP
- DISABLE TOILET ALARM
- ASPIRATING SMOKE DETECTOR
- AOV PANEL

- GAS ALARM PANEL
- IP65 EXTERNAL SOUNDER WITH BEACON
- DISABLED REFUGE CALL POINT
- HEAT TAPE
- HEAT TAPE INTERFACE

- STATIC DOME CCTV CAMERA
- FIXED CCTV CAMERA
- AUDIO INTERCOM SYSTEM

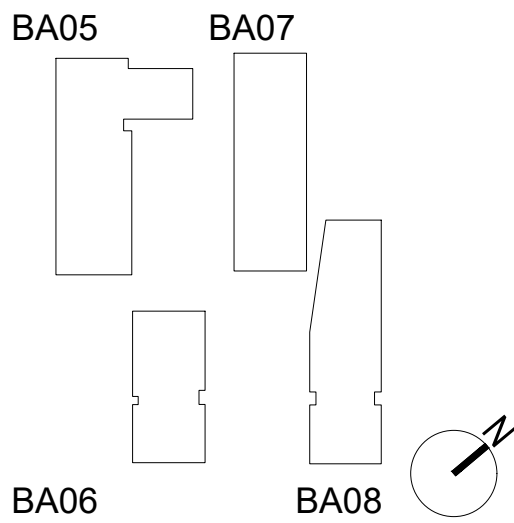

Rev	Date	Description	Orig	App
00	15.05.26	ISSUED FOR TENDER	RU	VU

EDC
Cork Office
Tel: +353 (0)21 426476
Dublin Office
Tel: +353 (0)1 5115903
London Office
Tel: +44 (0)20 3040260
www.edcengineers.com

Mechanical & Electrical Consulting Engineers
email: info@edcengineers.com
email: info@edcengineers.com
email: info@edcengineers.com

THIS DRAWING IS THE PROPERTY OF E.D.C. AND SHALL NOT BE USED, REPRODUCED OR DISCLOSED TO ANYONE WITHOUT THE PRIOR WRITTEN PERMISSION OF E.D.C. AND SHALL BE RETURNED UPON REQUEST.



RIBA Work Stage	Status Code	Current Revision
3,4	S2	00
Scale @ A1	Model Manager	Project Manager
1 : 100	BOL	JR

Client	GLENVEAGH HOMES
Project	FORD SITE CENTRE PARK ROAD CORK
Title	Podium PD02 - Fire Alarm and Security Services Layout - Level 00 - Sheet 3 Of 4
Drawing No	FRDPD02-EDC-65-00-DR-E-006503