


FIRE ALARM NOTES
1. THIS DRAWING IS TO BE READ IN CONJUNCTION WITH PROJECT SPECIFICATION(S) & ALL OTHER CONTRACT DOCUMENTATION & DRAWINGS AS ISSUED BY THE ARCHITECT, STRUCTURAL ENGINEER & CONSULTING ENGINEERS. 2. ALL DIMENSIONS IN MILLIMETERS UNLESS OTHERWISE STATED. 3. THE CONTRACTOR SHALL NOTE THAT THIS DRAWING IS INDICATIVE AND ILLUSTRATES DESIGN INTENT ONLY. THE CONTRACTOR SHALL BE RESPONSIBLE FOR THE DETAILED DESIGN AND COORDINATION WITH THE STRUCTURE AND OTHER SERVICES. 4. ANY DISCREPANCIES, ERRORS OR OMISSIONS ARE TO BE CLARIFIED WITH THE RELEVANT ENGINEER AT THE EARLIEST OPPORTUNITY. 5. ALL WORKS ARE TO BE IN ACCORDANCE WITH THE CURRENT RELEVANT REGULATIONS, BUILDING REGULATIONS, IRISH STANDARDS, ACCEPTED CODES OF PRACTICE & TRADE ASSOCIATION REQUIREMENTS. 6. IT IS THE ELECTRICAL CONTRACTOR'S RESPONSIBILITY TO LIAISE WITH THE MAIN CONTRACTOR & ALL OTHER TRADES TO ENSURE THE CO-ORDINATION OF WORKS TO SUIT PROGRAM CONTRACTS & AVOID CLASHES. 7. THE ELECTRICAL CONTRACTOR SHALL PROVIDE ALL NECESSARY SUPPORTS & MOUNTING ACCESSORIES. 8. ALL ELECTRICAL INSTALLATIONS SHALL COMPLY WITH THE CURRENT IS10101 WIRING REGULATIONS. 9. CONDUIT RUNS SHALL BE SIZES AND CONFIRMED BY THE ELECTRICAL CONTRACTOR IN ACCORDANCE WITH THE CURRENT IS 10101 WIRING REGULATIONS. 10. CONTRACTOR TO CONFIRM THAT THE FIRE ALARM DESIGNS COMPLIES WITH IS 3218:2019. 11. ALL HEIGHT AND LOCATIONS OFF ALL ELECTRICAL OUTLETS TO BE CONFIRMED WITH ARCHITECT PRIOR TO INSTALLATION. 12. ALL DRAWINGS TO COMPLY WITH PART M OF THE BUILDING REGULATIONS. 13. VOICE EVACUATION ALARM SYSTEM TO BE DESIGNED BY SPECIALIST. PLEASE SEE PARTICULAR SCOPE OF WORKS AND SCHEMATICS FOR MORE DETAIL.
SECURITY & ACCESS CONTROL NOTES
1. THIS DRAWING IS TO BE READ IN CONJUNCTION WITH PROJECT SPECIFICATIONS(S) & ALL OTHER CONTRACT DOCUMENTATION & DRAWINGS AS ISSUED BY THE ARCHITECT, STRUCTURAL ENGINEER & CONSULTING ENGINEERS. 2. ALL DIMENSIONS IN MILLIMETERS UNLESS OTHERWISE STATED. 3. THE CONTRACTOR SHALL NOTE THAT THIS DRAWING IS INDICATIVE AND ILLUSTRATES DESIGN INTENT ONLY. THE CONTRACTOR SHALL BE RESPONSIBLE FOR THE DETAILED DESIGN AND COORDINATION WITH THE STRUCTURE AND OTHER SERVICES. 4. ANY DISCREPANCIES, ERRORS OR OMISSIONS ARE TO BE CLARIFIED WITH THE RELEVANT ENGINEER AT THE EARLIEST OPPORTUNITY. 5. ALL WORKS ARE TO BE IN ACCORDANCE WITH THE CURRENT RELEVANT REGULATIONS, BUILDING REGULATIONS, IRISH STANDARDS, ACCEPTED CODES OF PRACTICE & TRADE ASSOCIATION REQUIREMENTS. 6. IT IS THE ELECTRICAL CONTRACTOR'S RESPONSIBILITY TO LIAISE WITH THE MAIN CONTRACTOR & ALL OTHER TRADES TO ENSURE THE CO-ORDINATION OF WORKS TO SUIT PROGRAM CONTRACTS & AVOID CLASHES. 7. ANY DESIGN CHANGES OR DEVIATION FROM DESIGN MUST BE AGREED WITH THE CONSULTING ENGINEER. 8. ALL DIMENSIONS SHALL BE CHECKED ON SITE PRIOR TO FABRICATION ORDER OR DELIVERY. 9. FINAL DIMENSIONS SHALL BE CHECKED ON SITE PRIOR TO FABRICATION ORDER OR DELIVERY. 10. THE ELECTRICAL CONTRACTOR SHALL BE RESPONSIBLE FOR COORDINATION OF ALL SERVICES ON SITE. 11. THE ELECTRICAL CONTRACTOR SHALL BE RESPONSIBLE FOR PRODUCING A FULL SET OF COMBINED COORDINATED SERVICES DRAWINGS. 12. ALL DRAWINGS TO BE IN CONJUNCTION WITH ARCHITECTURAL DRAWINGS. 13. THE CONTRACTOR SHALL ALLOW FOR ALL NECESSARY SUPPORTS AND FITTINGS REQUIRED TO PROVIDE A FULLY FUNCTIONING INSTALLATION. 14. FINAL LOCATIONS OF ALL ACCESS CONTROL EQUIPMENT SUBJECT TO CONTRACTOR ARRANGING A SITE VISIT WITH SPECIALIST. 15. CCTV LOCATIONS SHOWN ARE INDICATIVE ONLY. CCTV SPECIALIST TO POSITION CAMERAS FOR BEST AREA COVERAGE BASED ON NUMBERS.

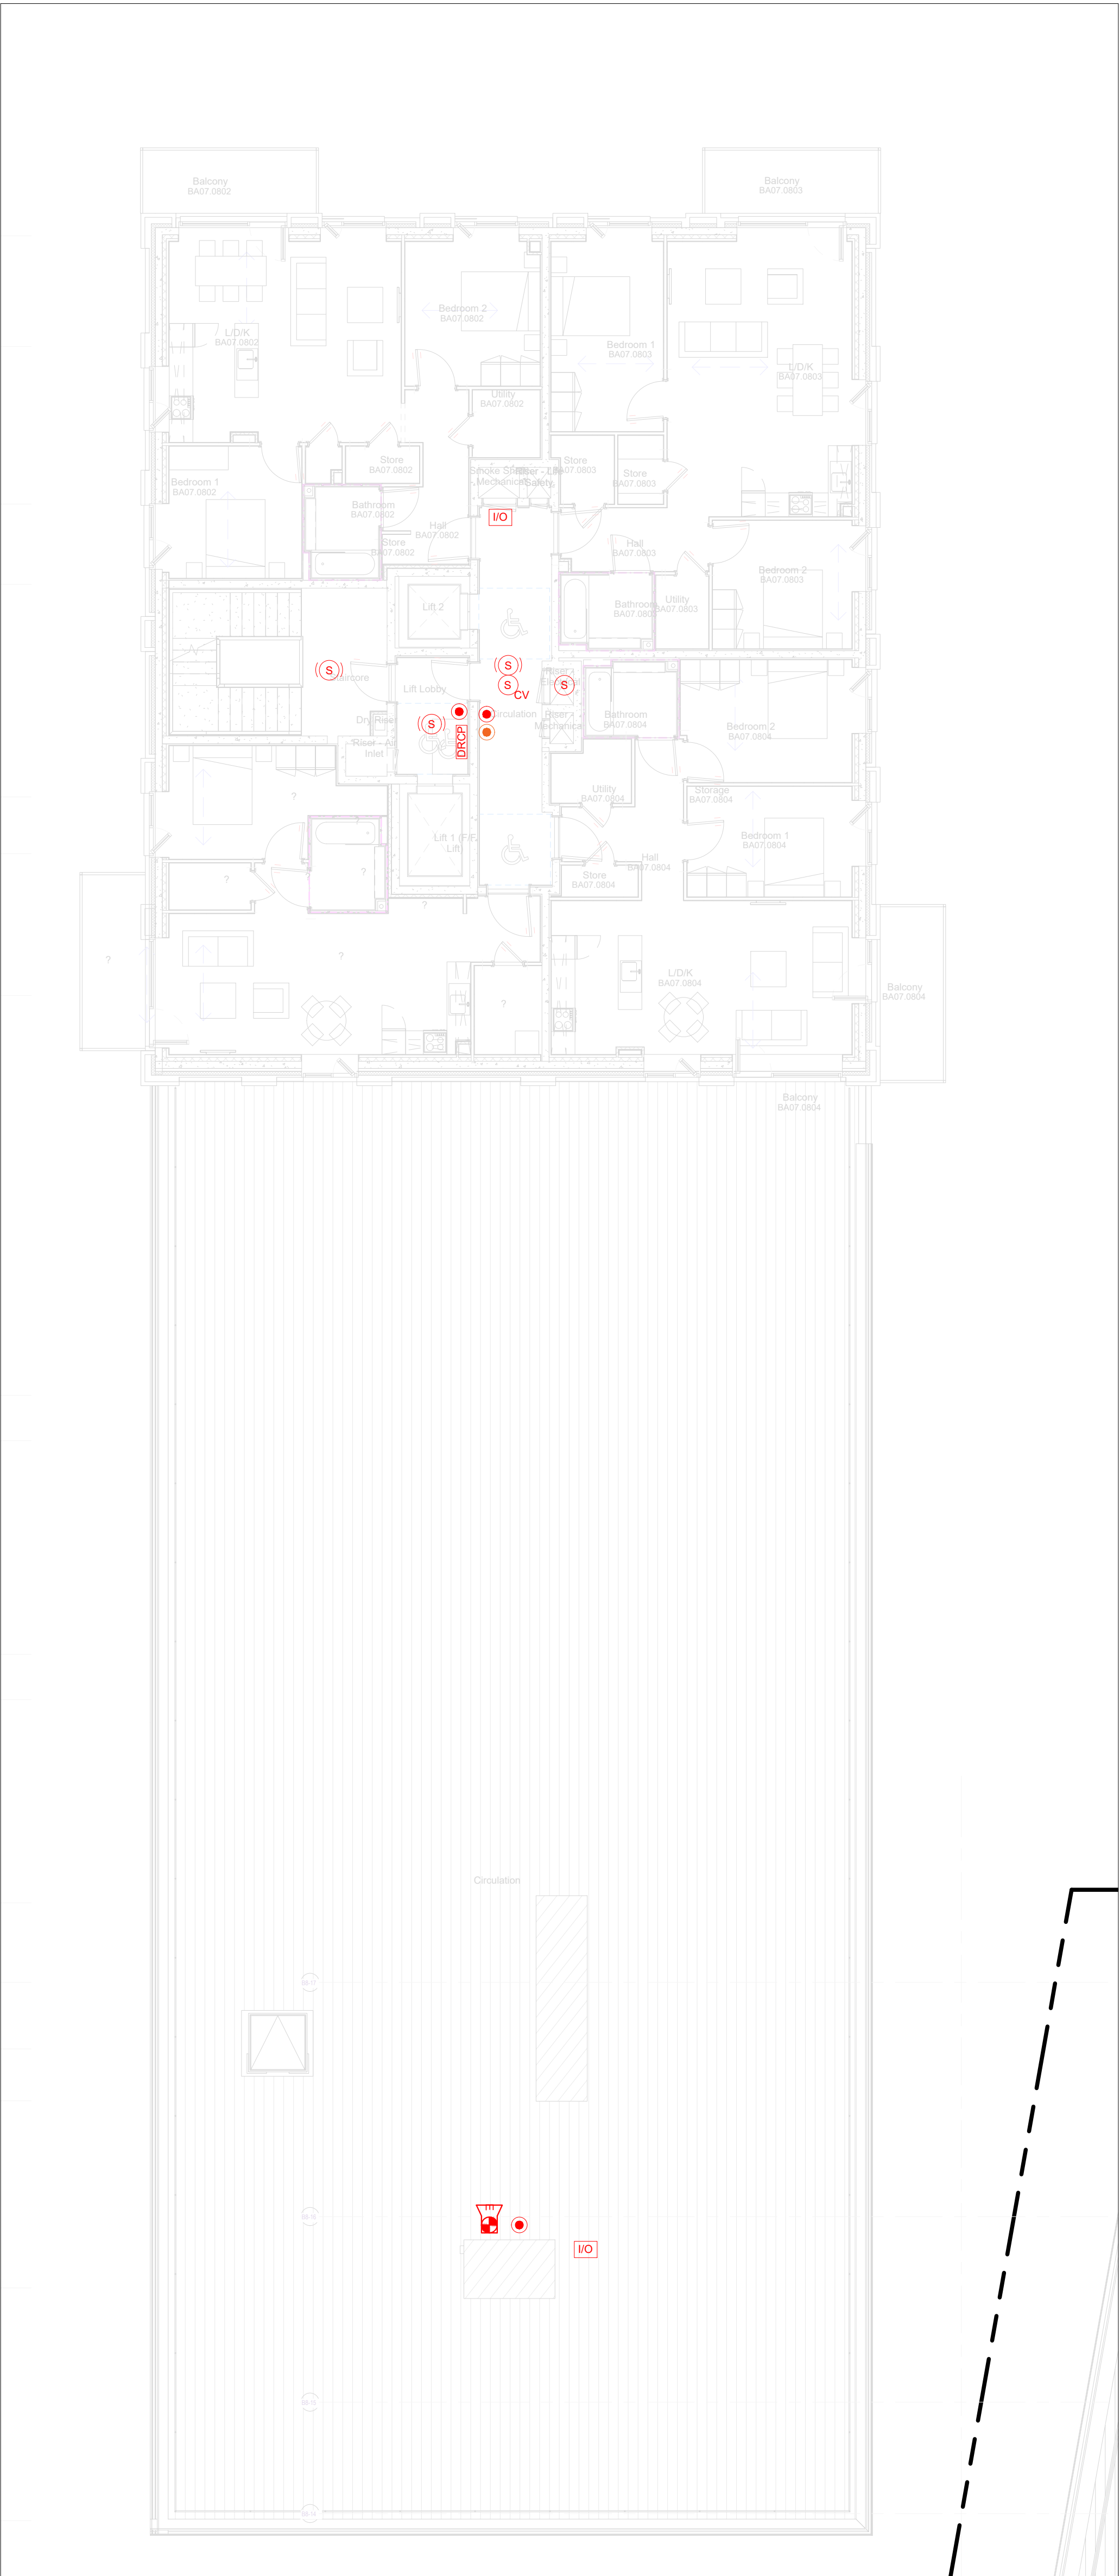

LEGEND
I/O INPUT OUTPUT DEVICES DRCP DISABLED REFUGE CALL POINT IP65 EXTERNAL SOUNDER WITH BEACON BREAK GLASS MANUAL CALL POINT FLASHING BEACON CO2 DETECTOR CO2 DETECTOR CV COMPLETE WITH REMOTE INDICATOR SMOKE DETECTOR HEAT DETECTOR SMOKE DETECTOR BEACON SMOKE DETECTOR CV COMPLETE WITH REMOTE INDICATOR HEAT DETECTOR CEILING VOID COMPLETE WITH REMOTE INDICATOR SMOKE SOUNDER HEAT DETECTOR SOUNDER HEAT DETECTOR BEACON SOUNDER SMOKE DETECTOR BEACON SOUNDER SOUNDER FLASHING BEACON FIRE ALARM REPEATER PANEL FIRE ALARM PANEL POWER SUPPLY UNIT EMERGENCY KNOCK OFF BUTTON GAS KNOCK OFF BUTTON BEAM DETECTOR DEAF ALTER TRANSMISSION FIRE ALARM SOUNDER GAS DETECTOR GAS ALARM PANEL DISABLE PULLOORD DISABLE ALARM RESET OVERDOOR INDICATOR LAMP DISABLE TOILET ALARM EMERGENCY POWER OFF AOV CALL POINT AOV PANEL ASPIRATING SMOKE DETECTOR FIRE SMOKE CURTAIN STATIC DOME CCTV CAMERA FIXED CCTV CAMERA AUDIO INTERCOM SYSTEM

BA05

BA07

BA06

BA08

Rev	Date	Description	Orig	App
00	22.04.26	ISSUED FOR INFORMATION	RU	VU
01	08.05.26	ISSUED FOR TENDER	RU	VU

Mechanical & Electrical Consulting Engineers

Cork Office

Tel: +353 (0)21 423476,

email: info@edcengineers.com

Dublin Office

Tel: +353 (0)1 513563,

email: info@edcengineers.com

London Office

Tel: +44 (0)20 344502,

email: info@edcengineers.com

www.edcengineers.com

THIS DRAWING IS THE PROPERTY OF E.D.C. AND SHALL NOT BE USED, REPRODUCED OR DISCLOSED TO ANYONE WITHOUT THE PRIOR WRITTEN PERMISSION OF E.D.C. AND SHALL BE RETURNED UPON REQUEST.

RIBA Work Stage

3,4

Status Code

S2

Current Revision

01

Scale @ A1

1 : 100

Model Manager

BOL

Project Manager

JR

Client

GLENVEAGH HOMES

Project

FORD SITE
CENTRE PARK ROAD CORK

Title

Block BA07 - Fire and Security Services Layout - Level 08-09

Drawing No

FRDBA07-EDC-65-ZZ-DR-E-006502