



FIRE ALARM NOTES

1. THIS DRAWING IS TO BE READ IN CONJUNCTION WITH PROJECT SPECIFICATION(S) & ALL OTHER CONTRACT DOCUMENTATION & DRAWINGS AS ISSUED BY THE ARCHITECT, STRUCTURAL ENGINEER & CONSULTING ENGINEERS.
2. ALL DIMENSIONS IN MILLIMETERS UNLESS OTHERWISE STATED.
3. THE CONTRACTOR SHALL NOTE THAT THIS DRAWING IS INDICATIVE AND ILLUSTRATES DESIGN INTENT ONLY. THE CONTRACTOR SHALL BE RESPONSIBLE FOR THE DETAILED DESIGN AND COORDINATION WITH THE STRUCTURE AND OTHER SERVICES.
4. ANY OMISSIONS, ERRORS OR OMISSIONS ARE TO BE CLARIFIED WITH THE RELEVANT ENGINEER AT THE EARLIEST OPPORTUNITY.
5. ALL WORKS ARE TO BE IN ACCORDANCE WITH THE CURRENT RELEVANT REGULATIONS, BUILDING REGULATIONS, IRISH STANDARDS, ACCEPTED CODE OF PRACTICE & CODE OF ASSOCIATION REQUIREMENTS.
6. IT IS THE ELECTRICAL CONTRACTOR'S RESPONSIBILITY TO LIAISE WITH THE MAIN CONTRACTOR & ALL OTHER TRADES TO ENSURE THE CO-ORDINATION OF WORKS TO SUIT PROGRAM CONTRACTS & AVOID CLASHES.
7. THE ELECTRICAL CONTRACTOR SHALL PROVIDE ALL NECESSARY SUPPORTS & MOUNTING ACCESSORIES.
8. ALL ELECTRICAL INSTALLATIONS SHALL COMPLY WITH THE CURRENT IS10101 WIRING REGULATIONS.
9. CONDUIT RUNS SHALL BE SIZES AND CONFIRMED BY THE ELECTRICAL CONTRACTOR IN ACCORDANCE WITH THE CURRENT IS 10101 WIRING REGULATIONS.
10. CONTRACTOR TO CONFIRM THAT THE FIRE ALARM DESIGNS COMPLIES WITH IS 3219:2010.
11. ALL HEIGHT AND LOCATIONS OFF ALL ELECTRICAL OUTLETS TO BE CONFIRMED WITH ARCHITECT PRIOR TO INSTALLATION.
12. ALL DRAWINGS TO COMPLY WITH PART M OF THE BUILDING REGULATIONS.
13. WORKMANSHIP TO BE IN ACCORDANCE WITH THE SPECIAL INSTRUCTIONS. PLEASE SEE PARTICULAR SCOPE OF WORKS AND SCHEMATICS FOR MORE DETAIL.

SECURITY & ACCESS CONTROL NOTES

1. THIS DRAWING IS TO BE READ IN CONJUNCTION WITH PROJECT SPECIFICATION(S) AND ALL OTHER CONTRACT DOCUMENTATION & DRAWINGS AS ISSUED BY THE ARCHITECT, STRUCTURAL ENGINEER & CONSULTING ENGINEER.
2. ALL DIMENSIONS IN MILLIMETERS UNLESS OTHERWISE STATED.
3. THE CONTRACTOR SHALL NOTE THAT THIS DRAWING IS INDICATIVE AND ILLUSTRATES DESIGN INTENT ONLY. THE CONTRACTOR SHALL BE RESPONSIBLE FOR THE DETAILED DESIGN AND COORDINATION WITH THE STRUCTURE AND OTHER SERVICES.
4. ANY DISCREPANCIES, ERRORS OR OMISSIONS ARE TO BE CLARIFIED WITH THE CONSULTING ENGINEER.
5. ALL WORKS ARE TO BE IN ACCORDANCE WITH THE CURRENT RELEVANT REGULATIONS, BUILDING REGULATIONS, IRISH STANDARDS, ACCEPTED CODES OF PRACTICE & TRADE ASSOCIATION REQUIREMENTS.
6. IT IS THE ELECTRICAL CONTRACTOR'S RESPONSIBILITY TO CO-ORDINE WITH THE MAIN CONTRACTOR & ALL OTHER TRADES TO ENSURE THE CO-ORDINATION OF WORKS TO SUIT PROGRAM CONTRACTS & AVOID CONFLICTS.
7. ANY DESIGN CHANGES OR DEVIATION FROM DESIGN MUST BE AGREED WITH THE CONSULTING ENGINEER.
8. ALL DIMENSIONS SHALL BE CHECKED ON SITE PRIOR TO FABRICATION ORDER OR DELIVERY.
9. FINAL DIMENSIONS SHALL BE CHECKED ON SITE PRIOR TO FABRICATION ORDER OR DELIVERY.
10. THE ELECTRICAL CONTRACTOR SHALL BE RESPONSIBLE FOR COORDINATION OF ALL SERVICES ON SITE.
11. THE ELECTRICAL CONTRACTOR SHALL BE RESPONSIBLE FOR PRODUCING A FULL SET OF COORDINATION SERVICES DRAWINGS.
12. ALL DRAWINGS TO BE IN CONJUNCTION WITH ARCHITECTURAL DRAWINGS.
13. THE CONTRACTOR SHALL ALLOW FOR ALL NECESSARY SUPPORTS AND BRACING REQUIREMENTS FOR THE CABLES AND CABLE TRAY INSULATION.
14. FINAL LOCATIONS OF ALL ACCESS CONTROL EQUIPMENT SUBJECT TO CONTRACTOR ARRANGING A SITE VISIT WITH SPECIALIST.
15. CCTV LOCATIONS SHOWN ARE INDICATIVE ONLY CCTV SPECIALIST TO POSITION CAMERAS FOR BEST AREA COVERAGE BASED ON NUMBERS.

LEGEND	
	INPUT OUTPUT DEVICES
	DISABLED REFUGE CALL POINT
	IP65 EXTERNAL SOUNDER WITH BEACON
	BREAK GLASS MANUAL CALL POINT
	FLASHING BEACON
	CO2 DETECTOR
	CO2 DETECTOR CV COMPLETE WITH REMOTE INDICATOR
	SMOKE DETECTOR
	HEAT DETECTOR
	SMOKE DETECTOR BEACON
	SMOKE DETECTOR CV COMPLETE WITH REMOTE INDICATOR
	HEAT DETECTOR CEILING VOID COMPLETE WITH REMOTE INDICATOR
	SMOKE SOUNDER
	HEAT DETECTOR SOUNDER
	HEAT DETECTOR BEACON SOUNDER
	SMOKE DETECTOR BEACON SOUNDER
	SOUNDER FLASHING BEACON
	FIRE ALARM REPEATER PANEL
	FIRE ALARM PANEL
	POWER SUPPLY UNIT
	EMERGENCY KNOCK OFF BUTTON
	GAS KNOCK OFF BUTTON
	BEAM DETECTOR
	DEAF ALERT TRANSMISSION
	FIRE ALARM SOUNDER
	GAS DETECTOR
	GAS ALARM PANEL
	DISABLE PULLCORD
	DISABLE ALARM RESET
	OVERDOOR INDICATOR LAMP
	DISABLE TOILET ALARM
	EMERGENCY POWER OFF
	AOV CALL POINT
	AOV PANEL
	ASPIRATING SMOKE DETECTOR
	FIRE SMOKE CURTAIN
	STATIC DOME CCTV CAMERA
	FIXED CCTV CAMERA
	AUDIO INTERCOM SYSTEM

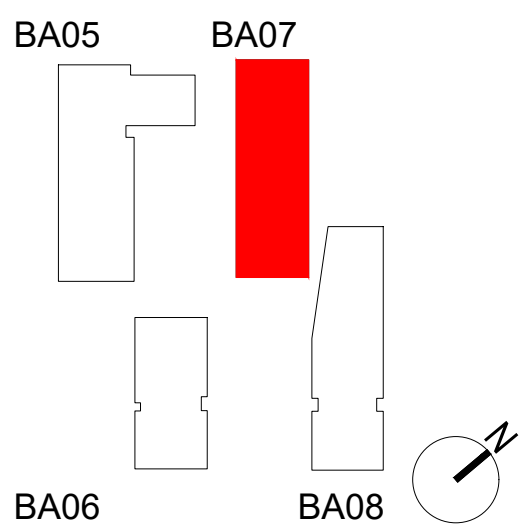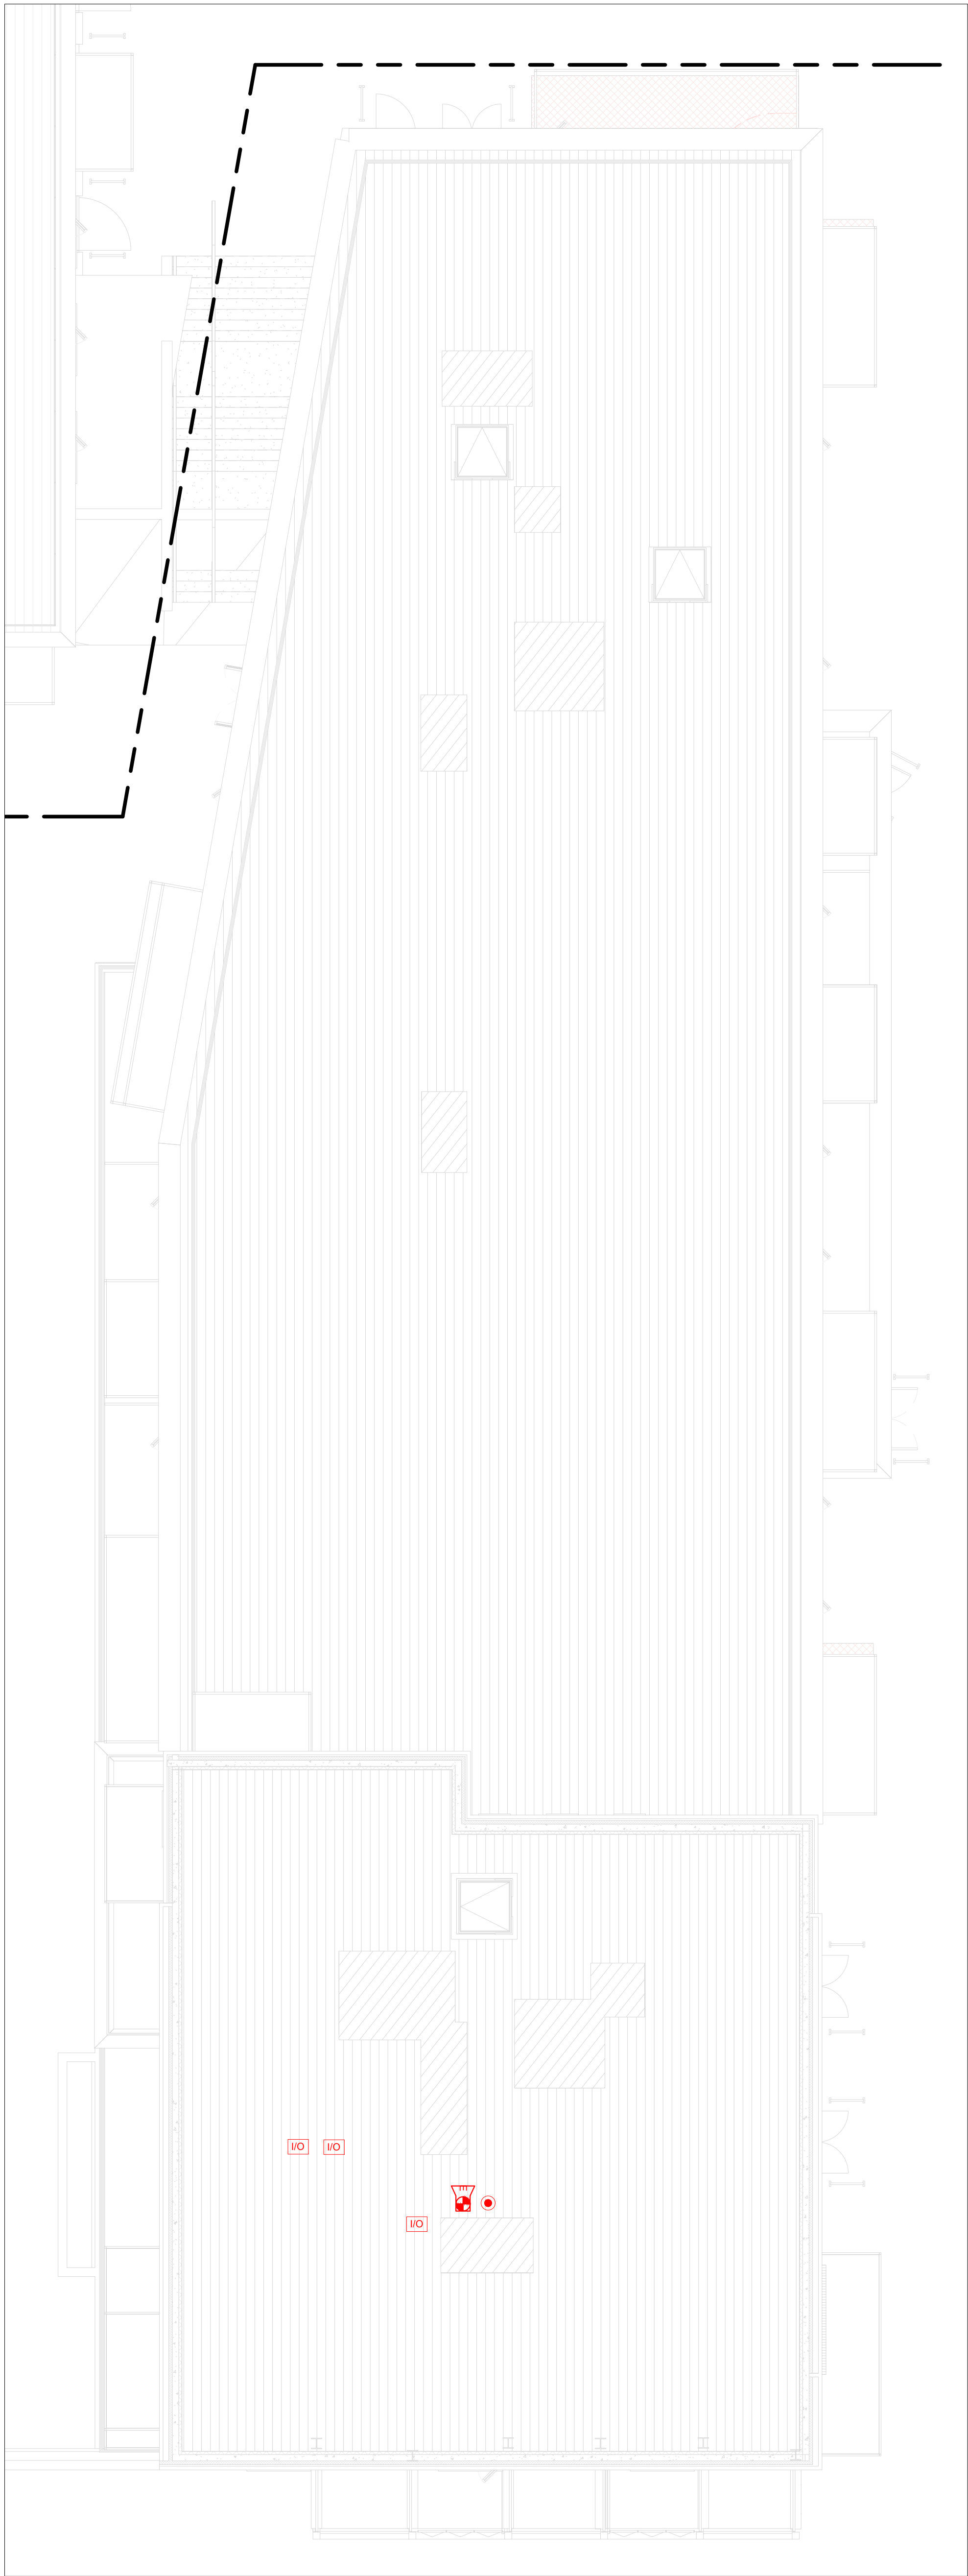

Rev	Date	Description	Orig	App
00	22.04.26	ISSUED FOR INFORMATION	RU	VU
01	08.05.26	ISSUED FOR TENDER	RU	VU



Cork Office
Tel: +353 (0)21 4280478, email: info@edcengineers.com

Dublin Office
Tel: +353 (0)1 5313683, email: info@edcengineers.com

London Office
Tel: +44 (0)203 0940062 email: info@edcengineers.com

www.edcengineers.com



RIBA Work Stage 3,4	Status Code S2	Current Revision 01
Scale @ A1 1 : 100	Model Manager BOL	Project Manager JR

Project FORD SITE
CENTRE PARK ROAD CORK

Title	Block BA08 - Fire and Security Services Layout - Roof Level
-------	--

Drawing No FRDBA08-EDC-65-RF-DR-E-006501